


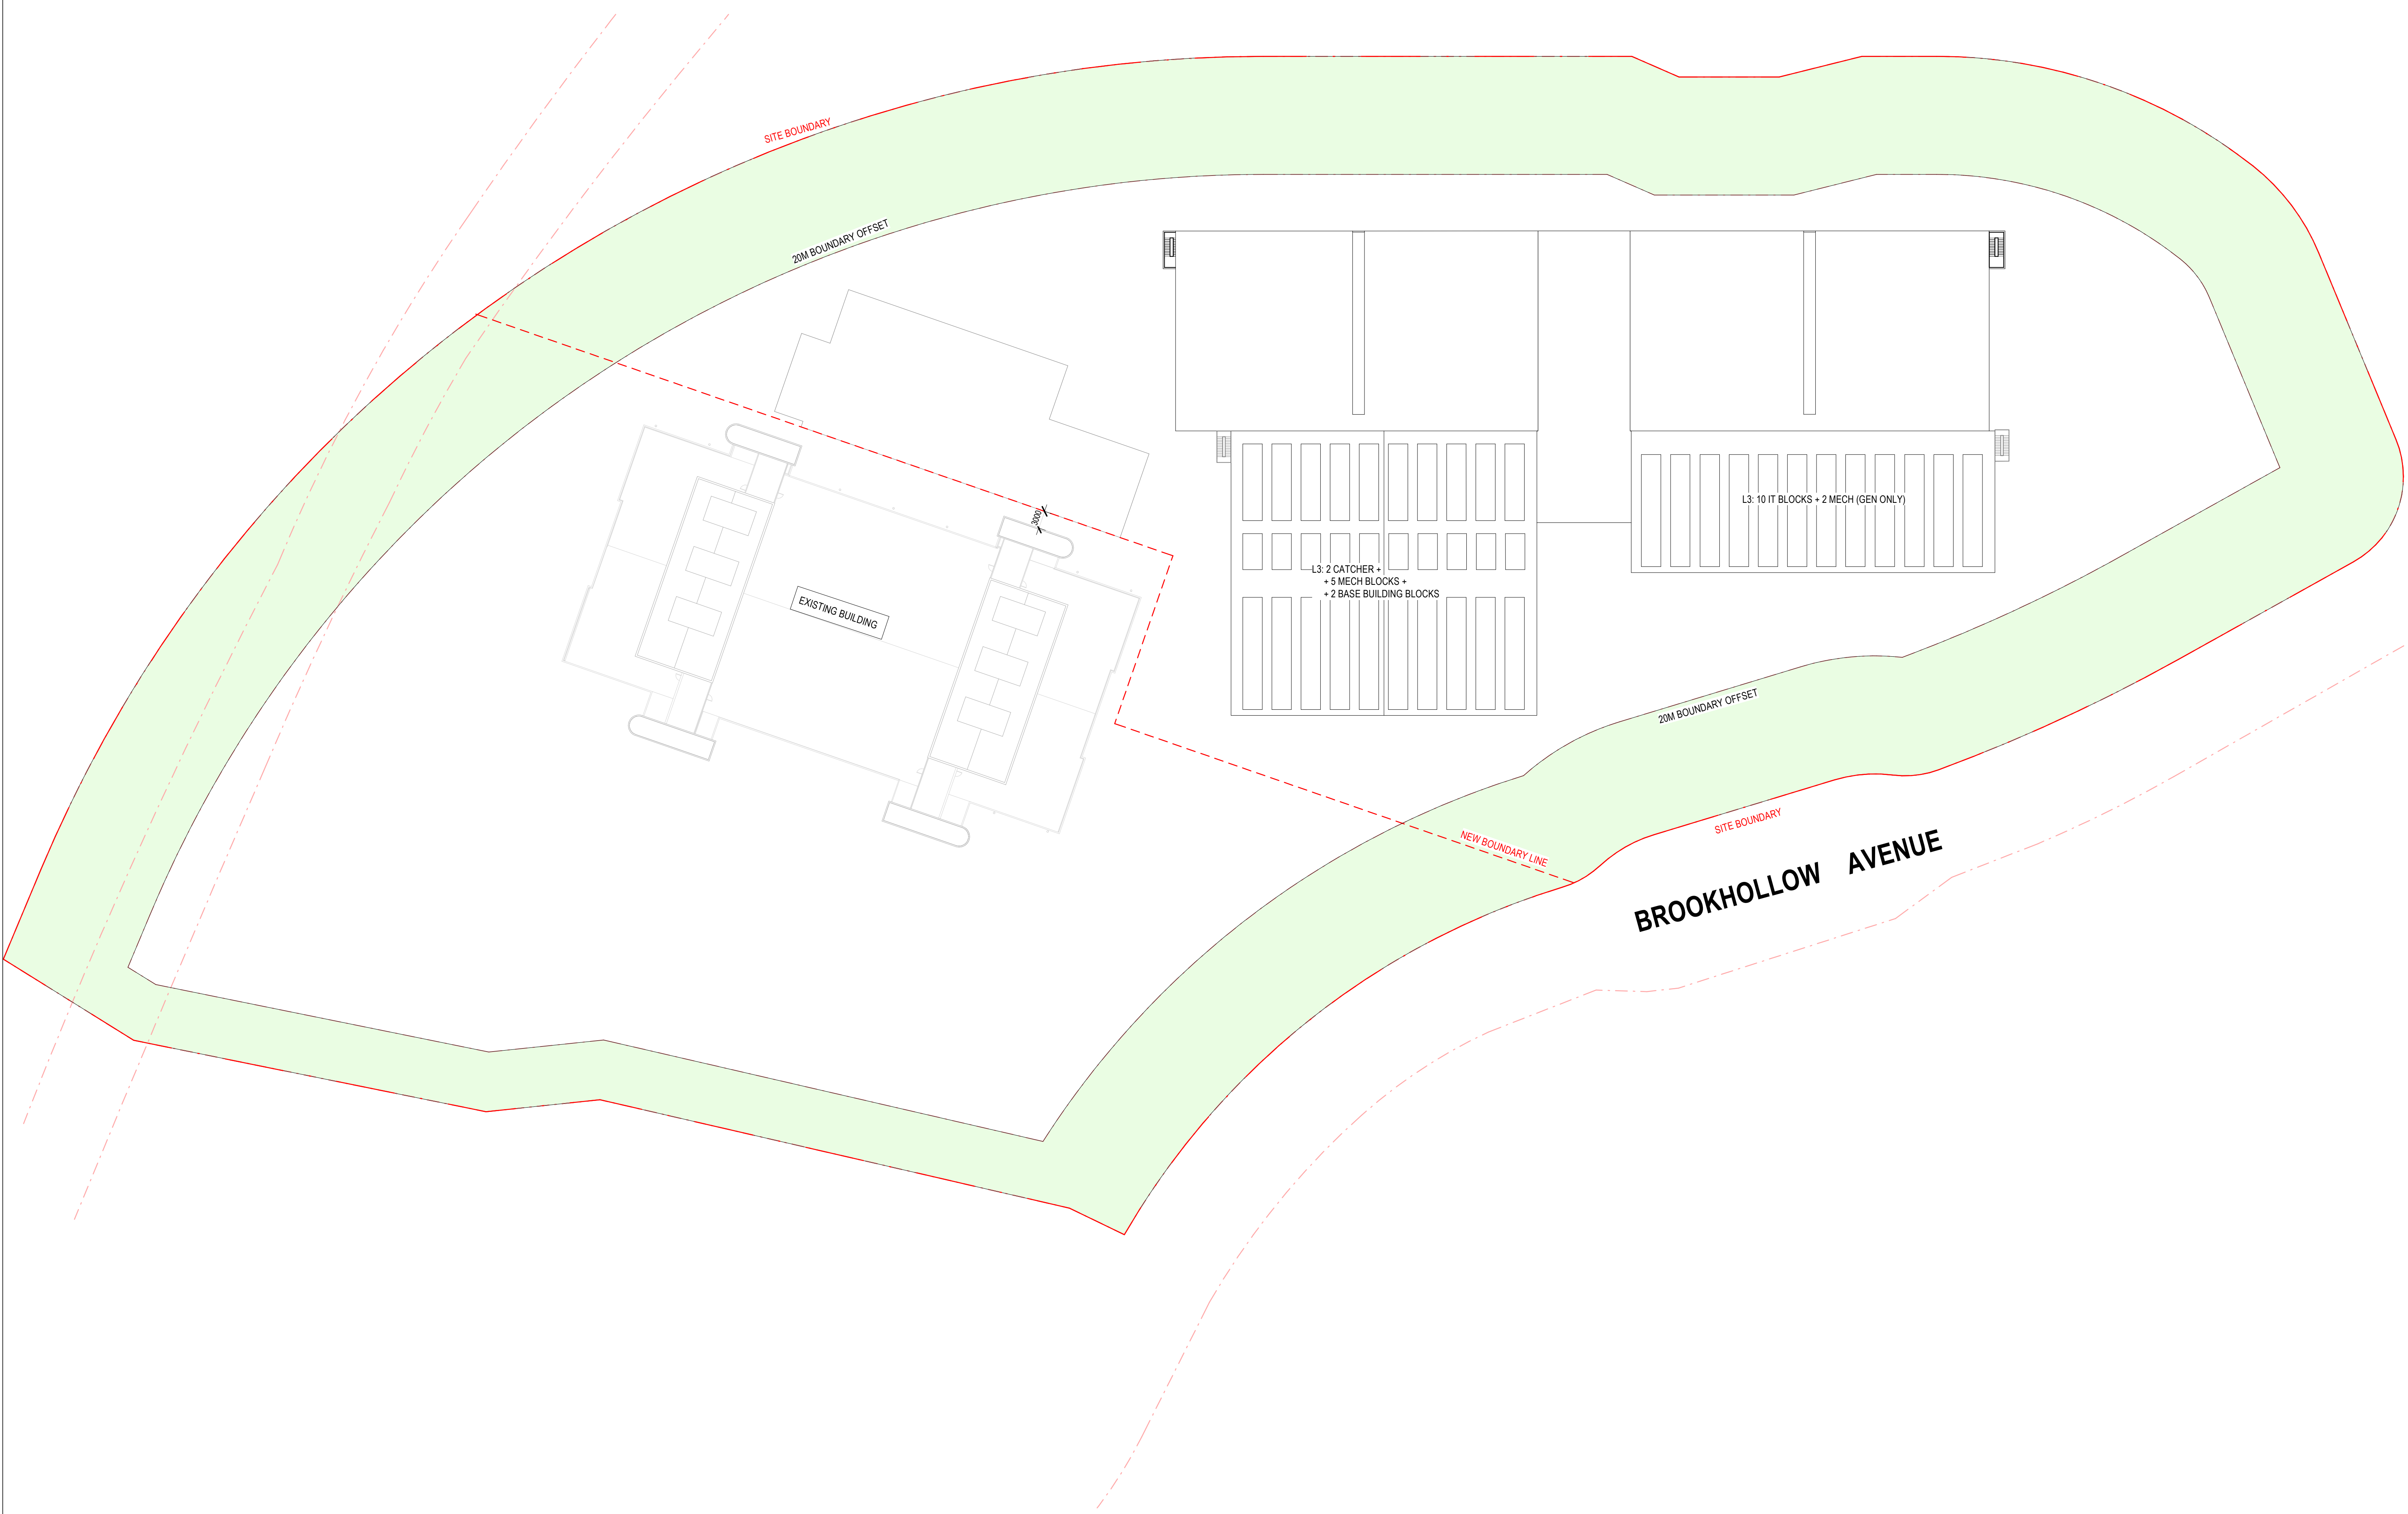

N	Issue		Date	Description ISSUED FOR INFORMATION ISSUED FOR INFORMATION	Key Plan	Project Manager		 A BGIS Company	 WHERE AI LIVES	 A WOOLPERT COMPANY +61 2 8069 8930 LEVEL 22 68 PITT STREET SYDNEY NSW 2000 AUSTRALIA GREENBOX ARCHITECTURE PTY LTD ABN: 79 139 779 098 ISO 9001 CERTIFIED QUALITY SYSTEM	Notes • Use written dimensions only • Do not scale from drawing • Contractors shall confirm all dimensions on-site prior to commencing any work or producing any shop drawings • All materials to be used in accordance with the manufacturer's specifications and instructions and shall comply with the relevant Australian Standards • Copyright of this drawing and design remain the property of Greenbox Architecture Pty Ltd • Nominated Architect - Gerard Page; NSW reg No.7247, Vic reg No.17664, QLD reg No.4538	Client GreenSquareDC™		Scale 1 : 500	Sheet A1	Scale Bar 1:500 0 5 10 15 25m
	1	2	19.11.2024 04.03.2025			Construction Manager						 RED ENGINEERING	Drawn By AE	Project Status PRELIMINARY		
	A1							Checked By EX	Drawing Title SYDGPU 2 - LEVEL 1 PLAN							
								Approved By GP	Project Norwest DC 3 Brookhollow Avenue Baulkham Hills NSW		Job Number 230062	Drawing Number ASK061	Issue 2			



<
--



<